


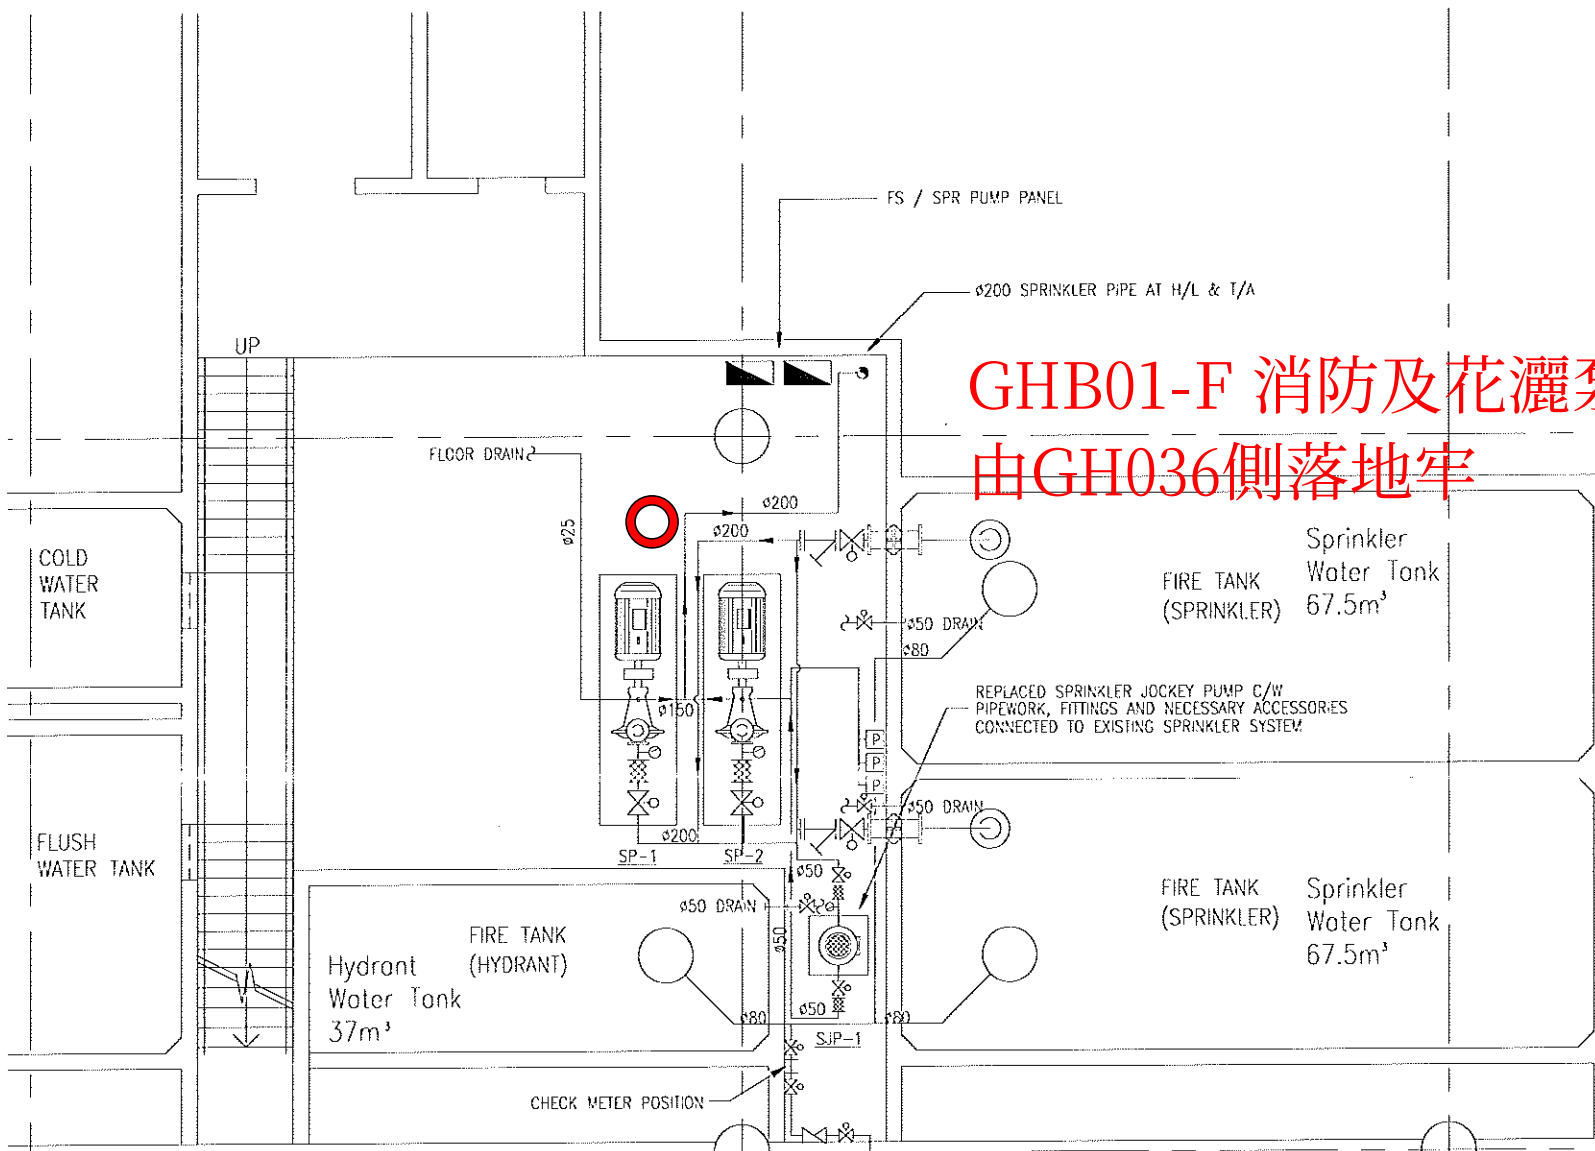

GHB01-F 消防及花灑泵 由GH036側落地牢